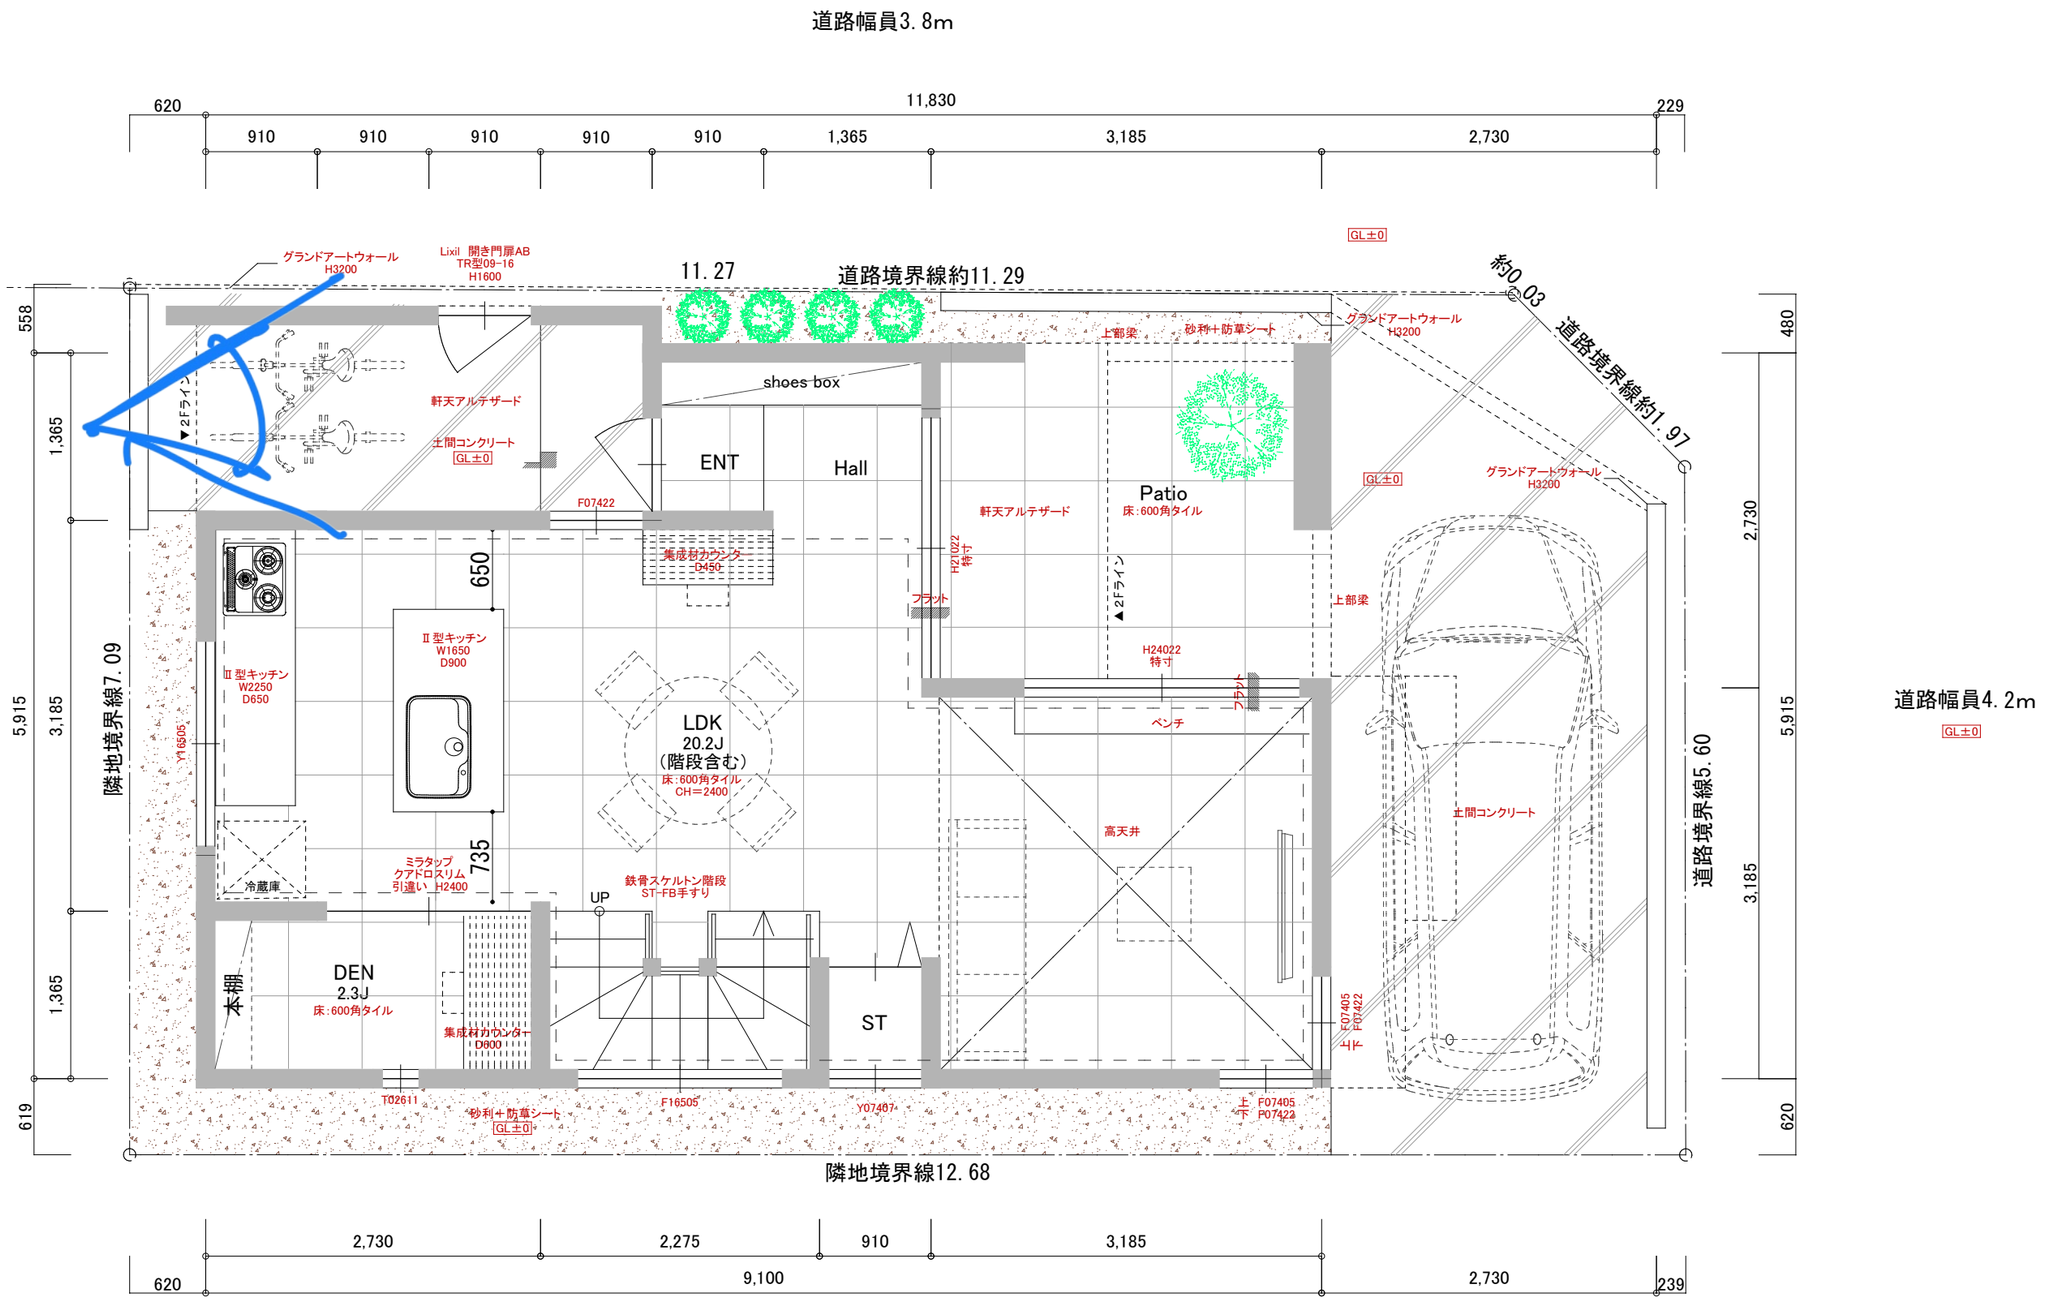

真北調査が必要です

※詳細な構造検討によりプラン変更が生じることがあります。
※敷地境界沿いの塀、フェンスは行政により改修指導がなされる場合があります。
※所管行政庁、他の所轄行政機関、確認申請機関等の指導等によりプラン変更が生じることがあります。
※隣地境界より建物の離れが 500mm以下の場合、民法第 234 条の規定により、隣地所有者に隣地近接承諾書へ署名捺印を頂く必要があります。

※当社で提示した図面、資料等をFREEDOM株式会社の承諾なしに複製・転用を含む使用を禁じます。
※建築予定地の現場調査、役所調査が未了の場合、プラン変更が生じることがあります。
※敷地測量が未了の場合、測量結果によりプラン変更が生じることがあります。

FREEDOM ARCHITECTS
FREEDOM株式会社　自由が丘スタジオ一級建築士事務所
自由が丘スタジオ：一級　東京都知事登録　第59647号
東京都目黒区自由が丘2-10-14 青木ビル 2F　TEL:03-5731-8521

DATE HISTORY	PROJECT NUMBER	PROJECT TITLE	MANAGER	PLANNER	DRAWN BY	DRAWING TITLE	SHEET No
	202※-2※-※※※	岡本直也様邸新築工事	藤井	高橋	内田	1階平面図	A－1
			DATE 2025.11.23				SCALE 1 / 50

※この資料をFREEDOM株式会社の承諾なしに、複製、転用を含む使用を禁ず。行政の指導によりプラン変更の可能性があります。

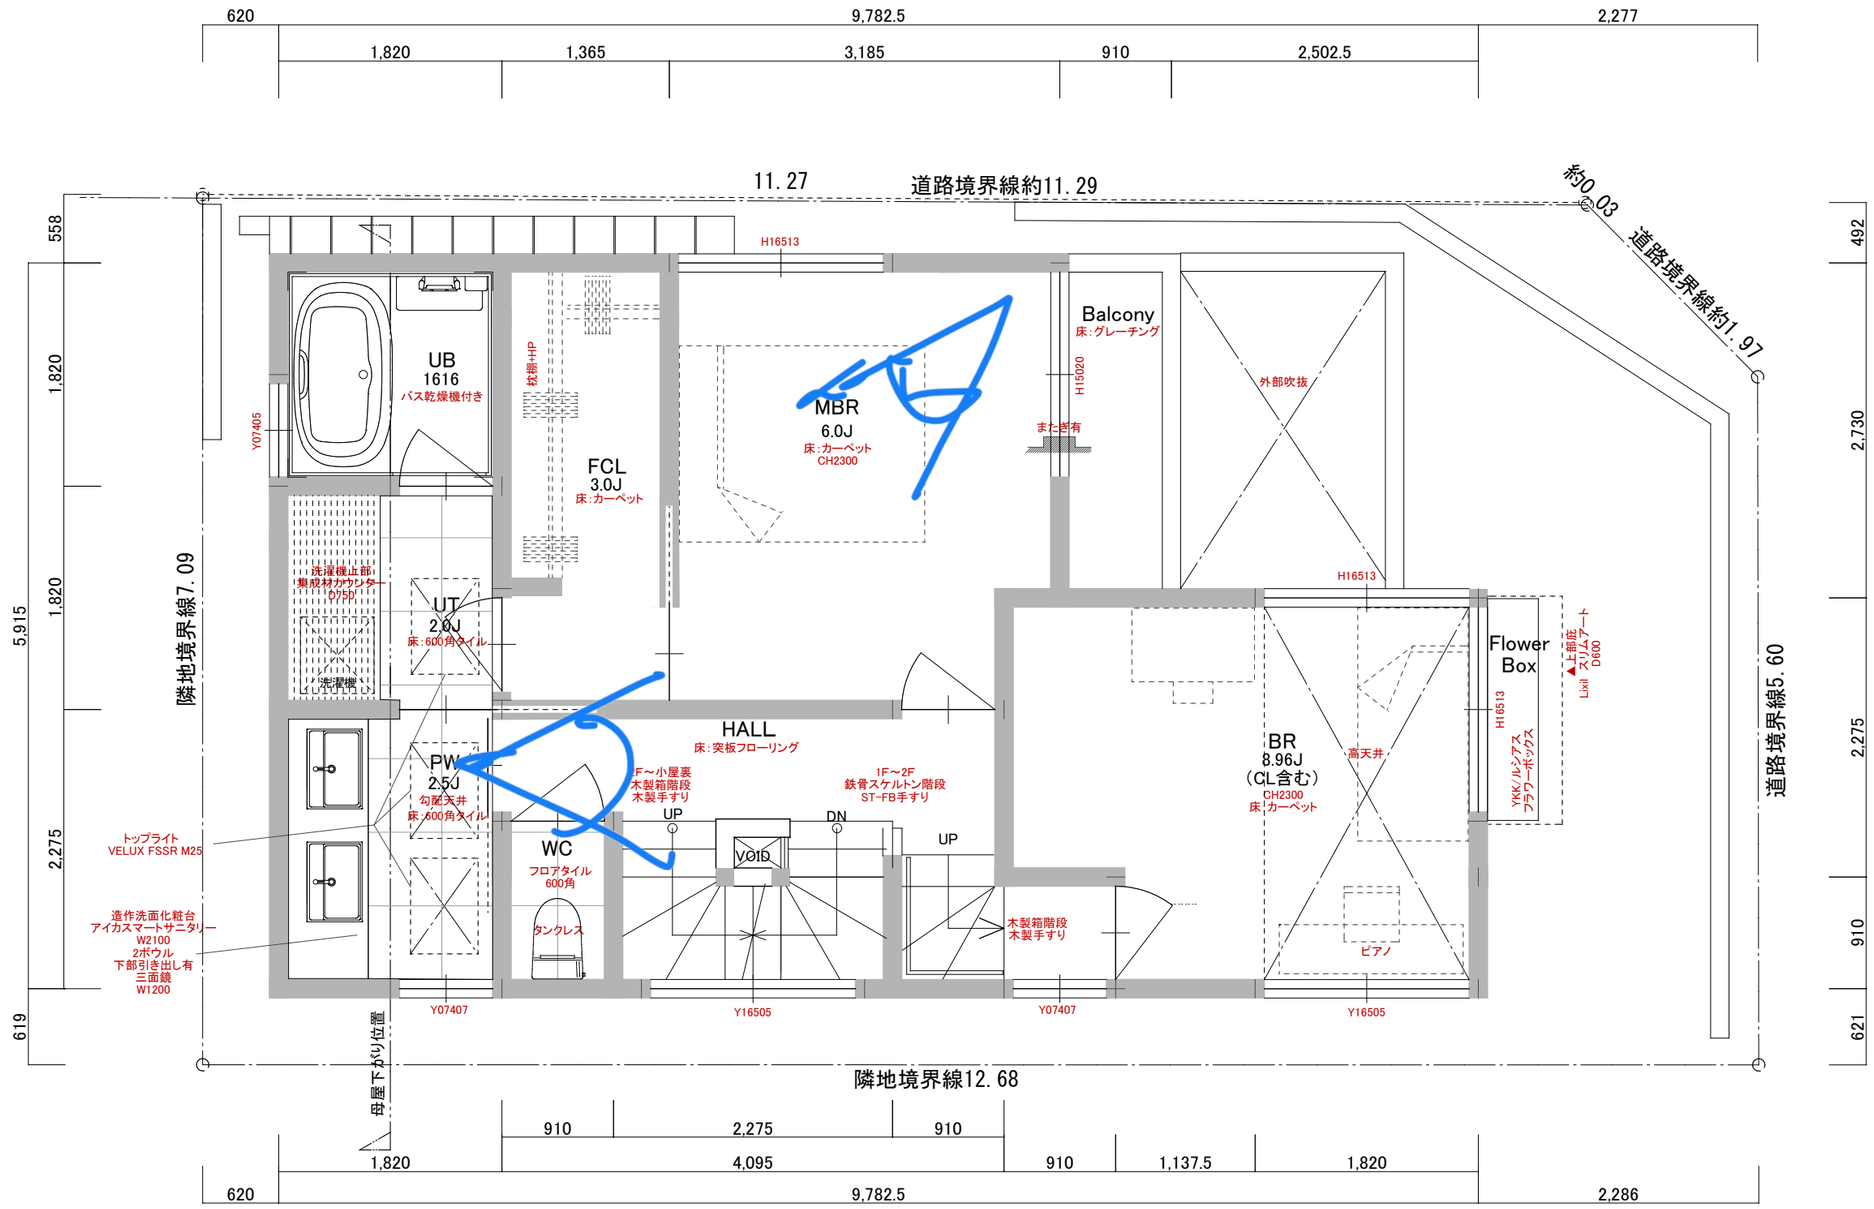

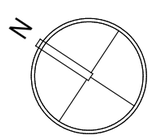

真北調査が必要です

※詳細な構造検討によりプラン変更が生じることがあります。
※敷地境界沿いの塀、フェンスは行政により改修指導がなされる場合があります。
※所管行政庁、他の所轄行政機関、確認申請機関等の指導等によりプラン変更が生じることがあります。
※隣地境界より建物の離れが 500mm以下の場合、民法第 234 条の規定により、隣地所有者に隣地近接承諾書へ署名捺印を頂く必要があります。

※当社で提示した図面、資料等をFREEDOM株式会社の承諾なしに複製・転用を含む使用を禁じます。
※建築予定地の現場調査、役所調査が未了の場合、プラン変更が生じることがあります。
※敷地測量が未了の場合、測量結果によりプラン変更が生じることがあります。

FREE DOM
FREEDOM ARCHITECTS
FREEDOM株式会社　自由が丘スタジオ一級建築士事務所
自由が丘スタジオ：一級　東京都知事登録　第59647号
東京都目黒区自由が丘2-10-14 青木ビル 2F　TEL:03-5731-8521

DATE HISTORY	PROJECT NUMBER	PROJECT TITLE	MANAGER	PLANNER	DRAWN BY	DRAWING TITLE	SHEET No
	202※-2※-※※※	岡本直也様邸新築工事	藤井	高橋	内田	2階平面図	A－2
			DATE 2025.11.23				SCALE 1 / 50

※この資料をFREEDOM株式会社の承諾なしに、複製、転用を含む使用を禁ず。行政の指導によりプラン変更の可能性があります。

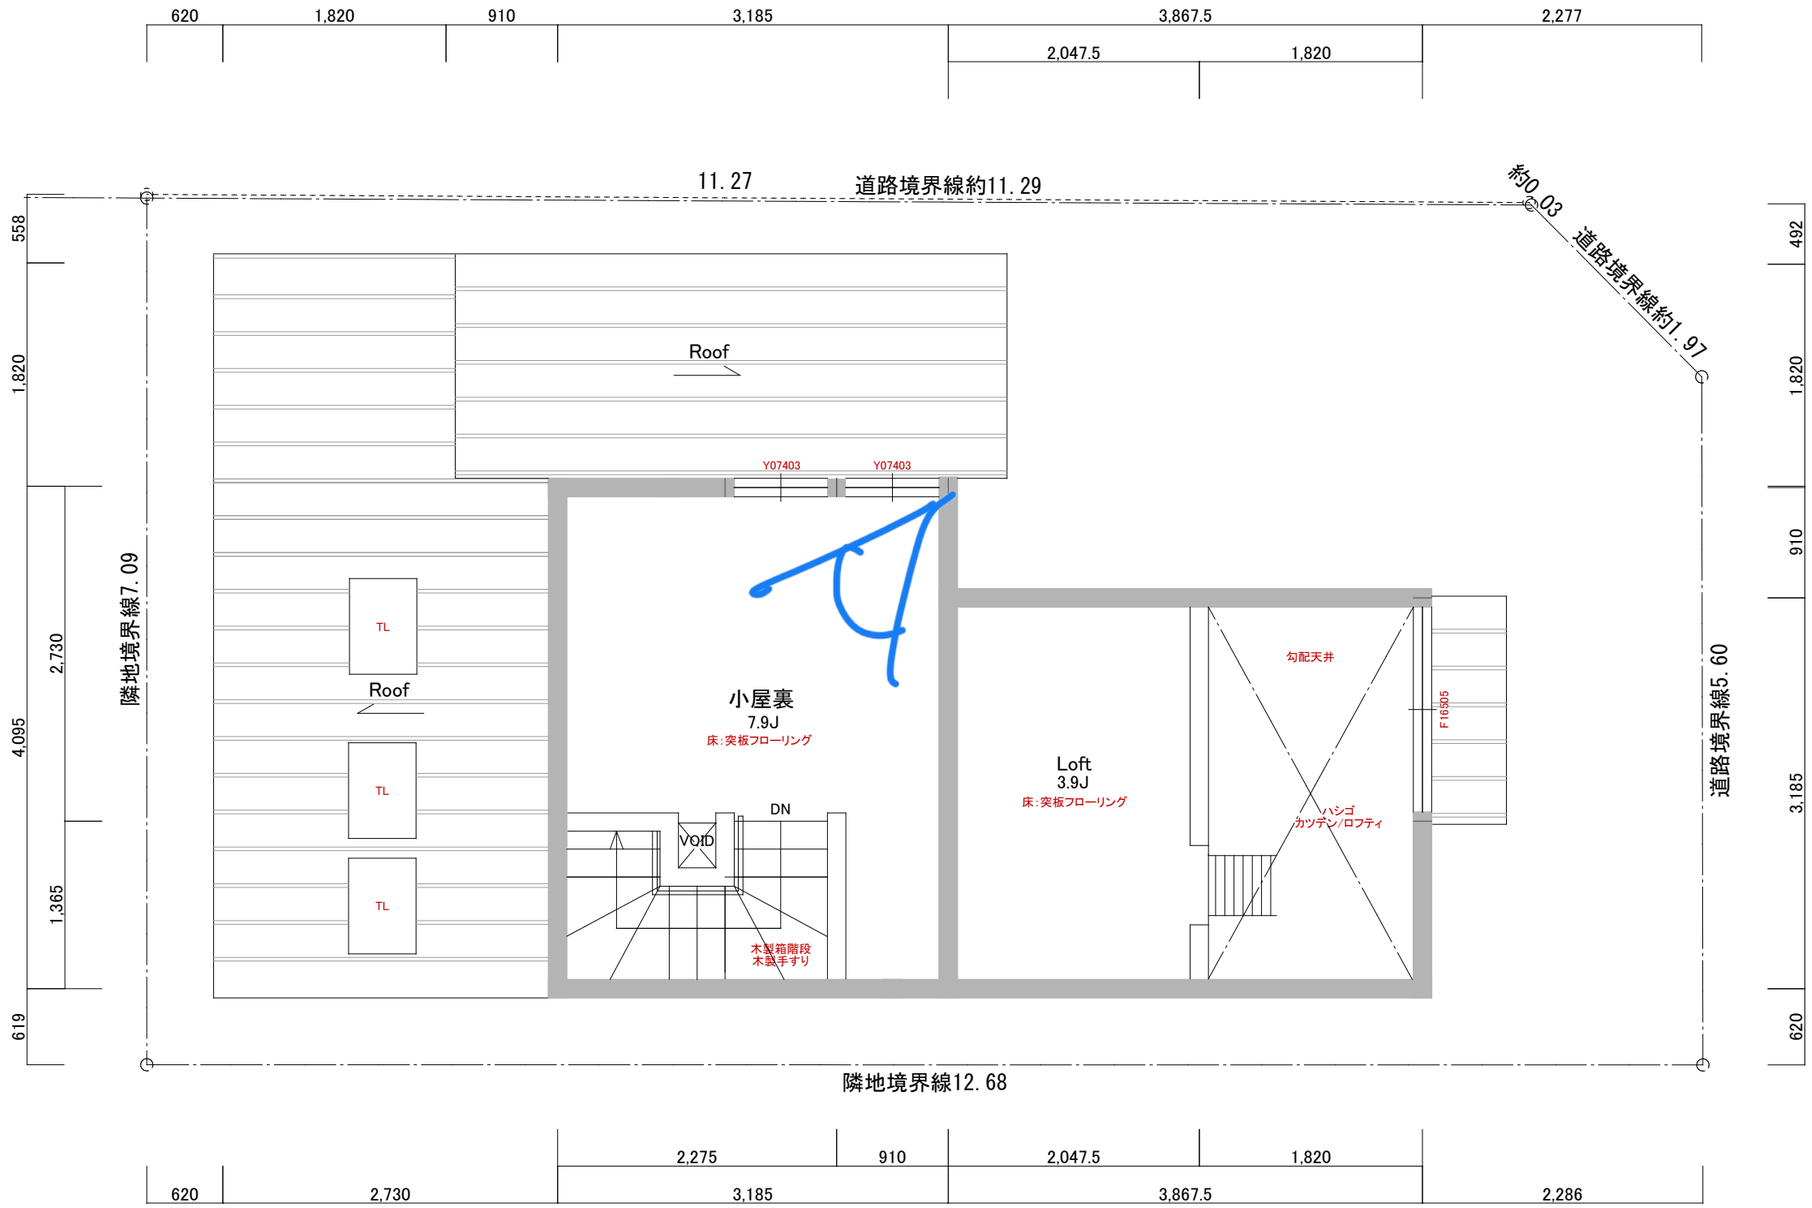

N

真北調査が必要です

※詳細な構造検討によりプラン変更が生じることがあります。
※敷地境界沿いの塀、フェンスは行政により改修指導がなされる場合があります。
※所管行政庁、他の所轄行政機関、確認申請機関等の指導等によりプラン変更が生じることがあります。
※隣地境界より建物の離れが 500mm以下の場合、民法第 234 条の規定により、隣地所有者に隣地近接承諾書へ署名捺印を頂く必要があります。

※当社で提示した図面、資料等をFREEDOM株式会社の承諾なしに複製・転用を含む使用を禁じます。
※建築予定地の現場調査、役所調査が未了の場合、プラン変更が生じることがあります。
※敷地測量が未了の場合、測量結果によりプラン変更が生じることがあります。

FREE DOM
FREEDOM ARCHITECTS
FREEDOM株式会社　自由が丘スタジオ一級建築士事務所
自由が丘スタジオ：一級　東京都知事登録　第59647号
東京都目黒区自由が丘2-10-14 青木ビル 2F　TEL:03-5731-8521

DATE HISTORY	PROJECT NUMBER	PROJECT TITLE	MANAGER	PLANNER	DRAWN BY	DRAWING TITLE	SHEET No
	202※-2※-※※※	岡本直也様邸新築工事	藤井	髙橋	内田	3階平面図	A－3
			DATE 2025.11.23				SCALE 1 / 50

※この資料をFREEDOM株式会社の承諾なしに、複製、転用を含む使用を禁ず。行政の指導によりプラン変更の可能性があります。